
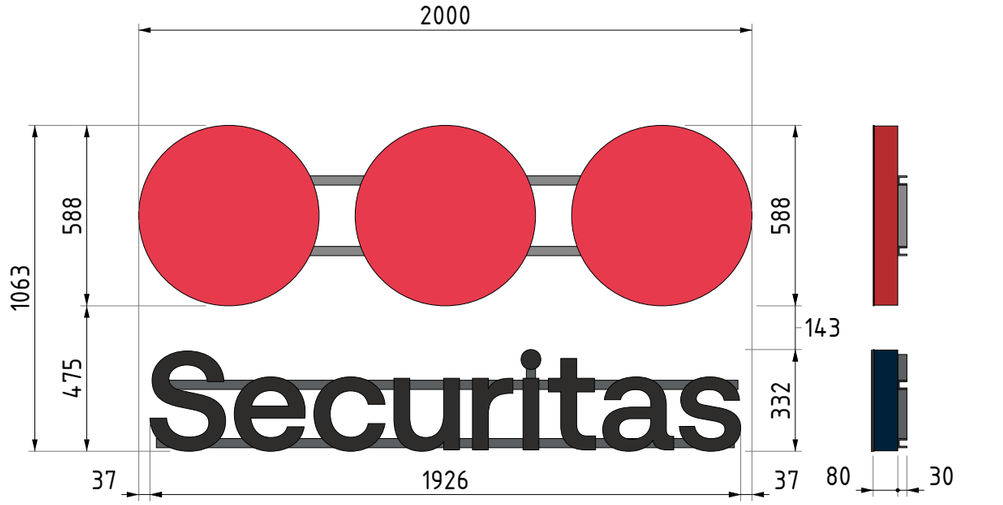



**FRONT VIEW**
SCALE 1:20

**SIDE VIEW (RIGHT)**
SCALE 1:20

Power / PSU / cable exits:

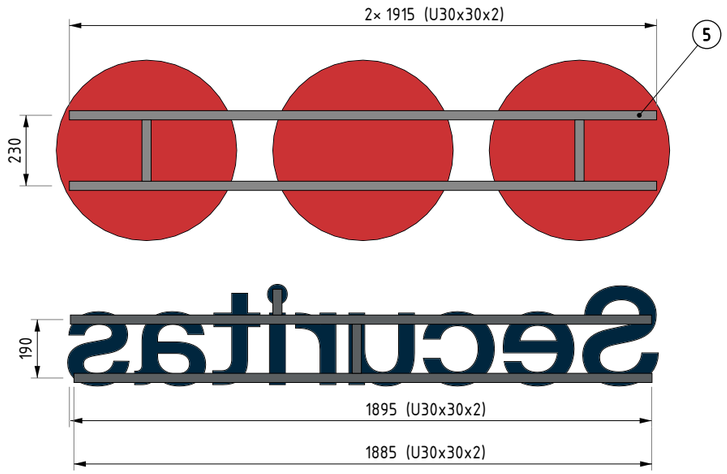



**REAR VIEW (MIRRORED)**
SCALE 1:20 | true view from the back





**3D VIEW**
ILLUSTRATIVE – NOT TO SCALE

**PROFILE 5S (CIRCLES)**

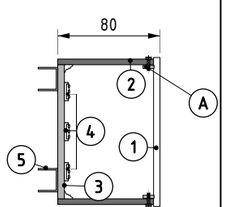


**PROFILE P6 (Securitas)**

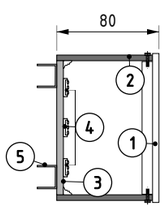


**BILL OF MATERIALS (per 1 pcs.)**

| POS | PART | MATERIAL | FINISH | QTY (PERIMETER / AREA) |
|---|---|---|---|---|
| 1 | Face 5S color (circles) | Plexiglas GS 3H67 red, 3 mm | – | 5.54 m / 0.81 $m^2$ |
| 1 | Face P6+foil (Securitas) | Acrylic 8 mm white | – | 10.78 m / 0.24 $m^2$ |
| | Front film day/night (Securitas) | day/night film black/white | – | 0.24 $m^2$ |
| A | Fitting PVC edge (circles) | PVC 3 mm | – | 5.54 m |
| B | Bolt, return to PVC edge | | – | |
| 2 | Return circles | Alu 1 mm | RAL 3028 | 5.54 m / 0.44 $m^2$ |
| 2 | Return Securitas | Alu 1 mm | PMS 2965 C | 10.78 m / 0.86 $m^2$ |
| 3 | Back circles | Alu 1.5 mm | RAL 3028 | 5.54 m / 0.81 $m^2$ |
| 3 | Back Securitas | Alu 1.5 mm | PMS 2965 C | 10.78 m / 0.24 $m^2$ |
| 4 | LED | LED | – | |
| 5 | Rail U 30x30x2 (circles) | Aluminium | ? (1080-M230 matt) | 4.23 m |
| 5 | Rail U 30x30x2 (Securitas) | Aluminium | NCS S 6005-R80B | 4.02 m |
| 7 | PSU | PSU | | |
| 8 | Wall fixing through U rails | | – | |

**MAIN DATA**

| | |
|---|---|
| Quantity | |
| Overall size | 2000 x 1063 |
| Profiles | 5S color / P6+foil |
| Depth | 80 |
| Face circles | Plexiglas GS 3H67 red, 3 mm |
| Face Securitas | Acrylic 8 white + day/night film |
| Returns | RAL 3028 / PMS 2965 C |
| Finish | semi matt / matt |
| Rails | U 30x30x2 Alu |
| Illumination | LED |
| Environment | Exterior |
| Weight (calc.) | ≈ 17 kg / pcs, excl. PSU |

**REVISIONS** ALL DIMENSIONS IN mm UNLESS OTHERWISE SPECIFIED

| REV | DESCRIPTION | DATE | BY |
|---|---|---|---|
| A | First issue | 2026-10-15 | |
| | | | |

CLIENT
**Securitas Sarpsborg**

TITLE
Securitas Sarpsborg 2000 x 1062 – 5S color + P6+foil on U rails

ORDER NO.
**ALT0000_00.00_RS**

FILE / DRAWING NO.
Securitas Sarpsborg

SCALE
1:20 / 1:20

FORMAT
A3

REV. A

PROJECTION

DATE
2026-10-15

Sheet 1 / 1