
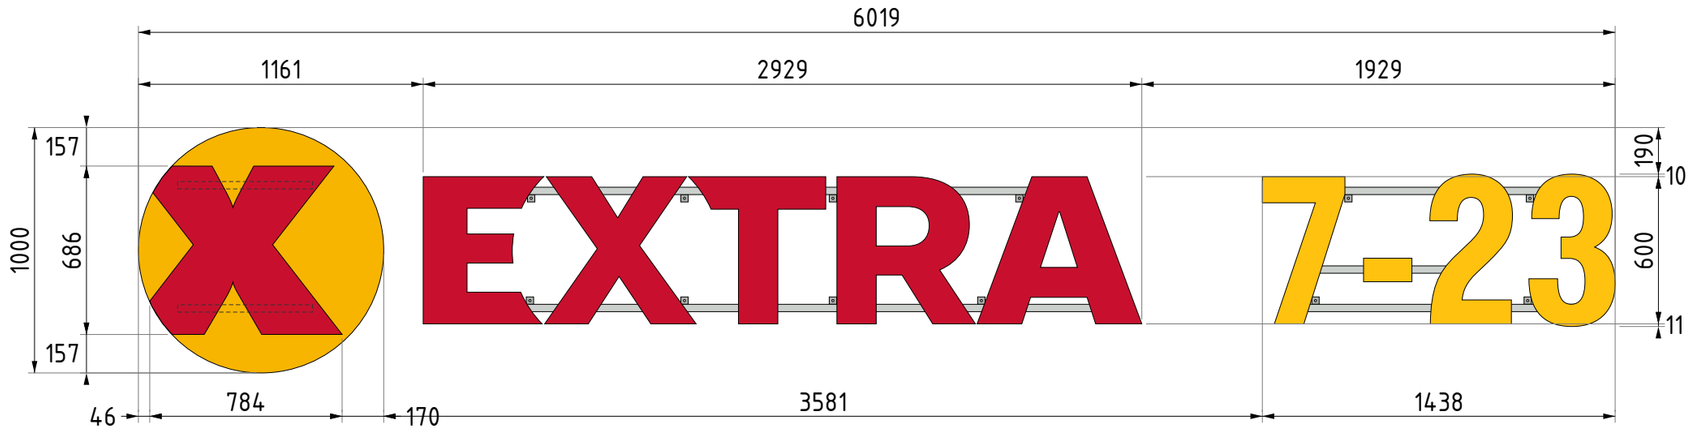


FRONT VIEW

SCALE 1:25

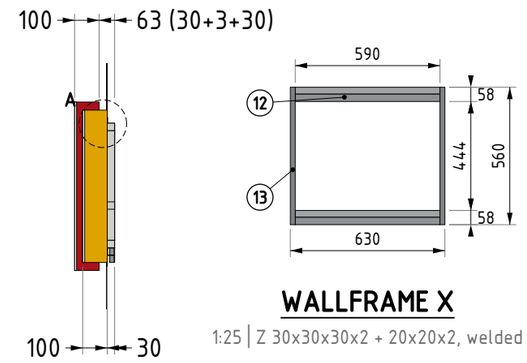


SIDE VIEW (RIGHT)

SCALE 1:25


WALLFRAME X

1:25 | Z 30x30x30x2 + 20x20x2, welded

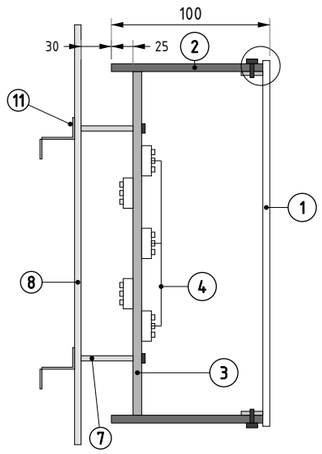

DETAIL A – SECTION

X – P6+3 ON ALU SHEET + Z HANG FRAME | SCHEMATIC

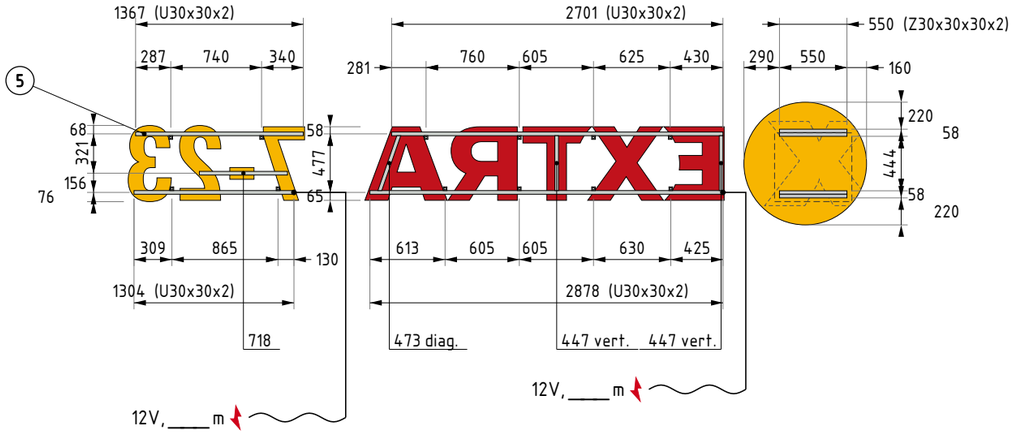

REAR VIEW (MIRRORED)


SCALE 1:50 | true view from the back



3D VIEW

ILLUSTRATIVE – NOT TO SCALE

PROFILE P6 ON RAILS – TYPICAL SECTION

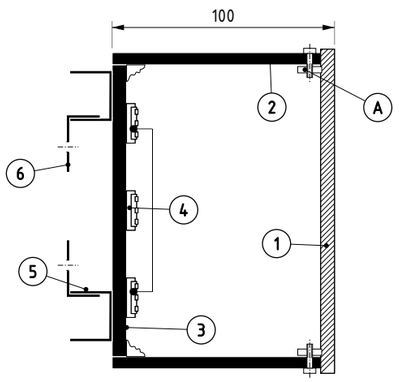

BILL OF MATERIALS (per 1 pcs.)

POS	PART	MATERIAL	FINISH	QTY (PERIMETER / AREA)
(1)	Letter face P6 (EXTRA, 7-23)	Plexi 3 mm white		22.17 m / 1.34 m²
(1)	Letter face P6+3 (X)	Plexi 3 mm white		3.54 m / 0.35 m²
	Front vinyl EXTRA + X	Vinyl foil, cast	3M 3630-33	0.98 + 0.35 m²
	Front vinyl 7-23	Vinyl foil, cast	3M 3630-125	0.36 m²
(A)	Fitting PVC edge	PVC 3 mm	-	25.71 m
(B)	Bolt, return to PVC edge		-	
(2)	Letter return EXTRA	Alu 1 mm	RAL 3020	14.63 m / 1.46 m²
(2)	Letter return 7-23	Alu 1 mm	RAL 1023	7.54 m / 0.75 m²
(2)	Letter return X	Alu 1 mm	RAL 3020	3.54 m / 0.35 m²
(3)	Letter back	Alu 1.5 mm	-	25.71 m / 1.68 m²
(4)	LED red / white 6500K		RED / 6500K	
(5)	Rail U 30x30x2 with ears (frame)	Aluminium	RAL 7035 matt	10.34 m
(6)	Mounting ear 30x30x2, ⌀6 hole	Aluminium	RAL 7035 matt	12 pcs. (0 extended)
(7)	Spacers 30 + 25 mm (X)		-	
(8)	Alu sheet ⌀1000 (X)	Alu 3 mm	RAL 1023	3.14 m / 0.78 m²
(9)	Trafo box, PWM + potentiometer			
(10)	Wall fixing		-	
(11)	Z strip 30x30x30x2 (on X sheet)	Alu	-	2 x 550 = 1.10 m
(12)	Wallframe Z 30x30x30x2	Alu		2 x 590 = 1.18 m
(13)	Wallframe tube 20x20x2	Alu		2 x 560 = 1.12 m

MAIN DATA

Quantity	
Overall size	6019 x 1000
Profiles	P6 (EXTRA, 7-23) / P6+3 (X)
Letter depth	100
Face	White plexi + 3M translucent
Returns	RAL 3020 / RAL 1023 (7-23)
Alu sheet	3 mm, RAL 1023
X sheet mount	Z strips + welded wallframe 630 x 560
Rails	U 30x30x2 + ears, RAL 7035 matt
Illumination	LED red / white 6500K, dimmable
Environment	Exterior
Weight (calc.)	≈ 34 kg / pcs, excl. PSU

REVISIONS

REV	DESCRIPTION	DATE	BY
A	First issue	2026-10-07	

CLIENT

BrandFactory

TITLE

Illuminated letters P6 on rails + P6+3 on alu sheet, Z hang frame

ORDER NO.	FILE / DRAWING NO.			
	EXTRA FAS 1000H100 (7-23)			
SCALE (DIM. mm)	FORMAT	SHEET	REV.	PROJECTION
1:25 / 1:50	A3	1 / 1	A	
DRAWN	CHECKED	DATE		
		2026-10-07		