
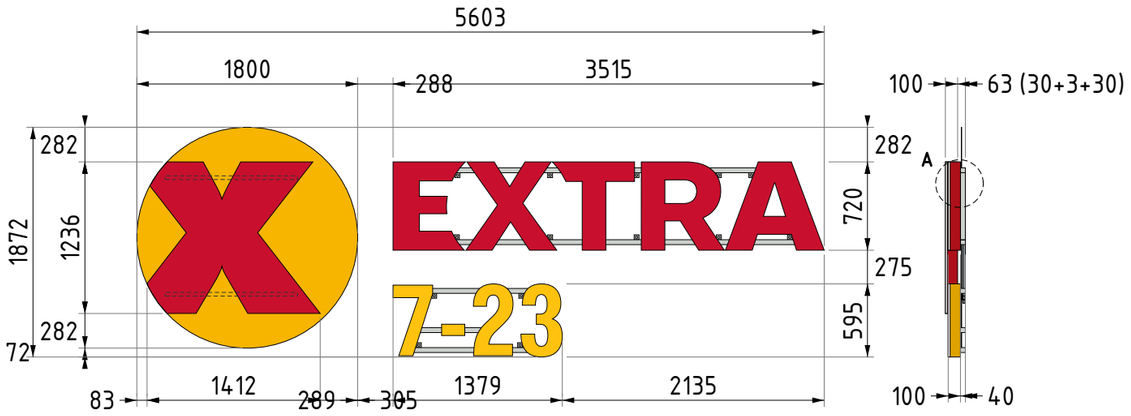


FRONT VIEW

SCALE 1:50


SIDE VIEW (RIGHT)

SCALE 1:50

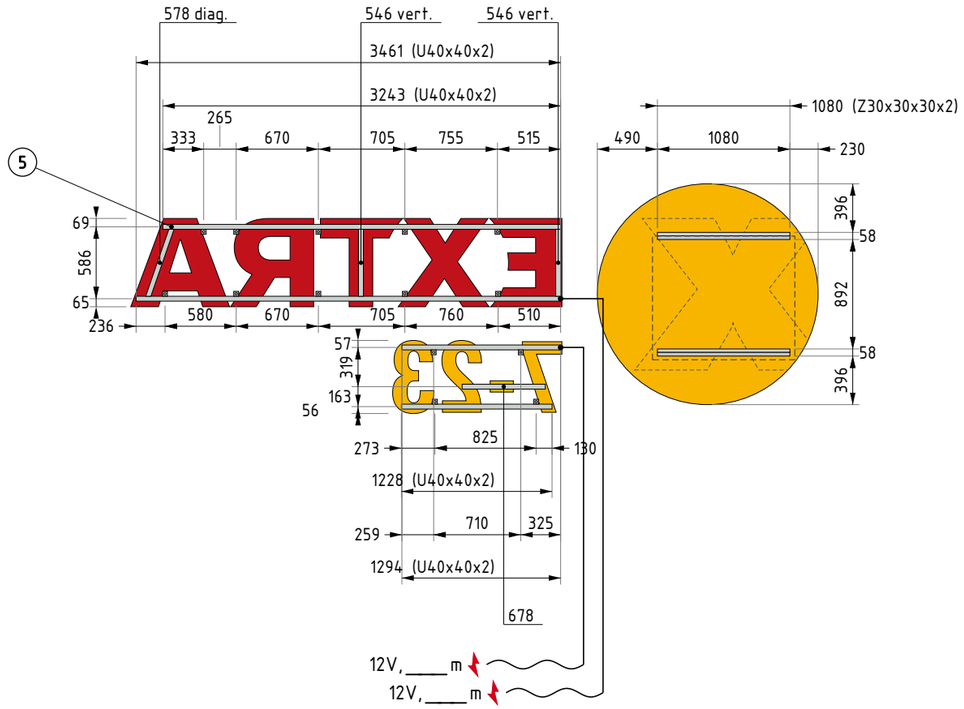

REAR VIEW (MIRRORED)

SCALE 1:50 | true view from the back

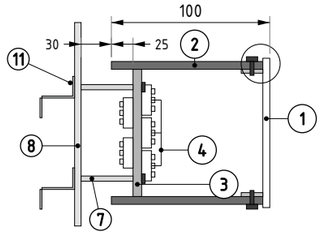


DETAIL A – SECTION

X – P6+3 ON ALU SHEET + Z HANG FRAME | SCHEMATIC



3D VIEW


ILLUSTRATIVE – NOT TO SCALE

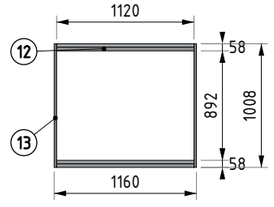

WALLFRAME X

1:50 | Z 30x30x30x2 + 20x20x2, welded

PROFILE P6 ON RAILS – TYPICAL SECTION

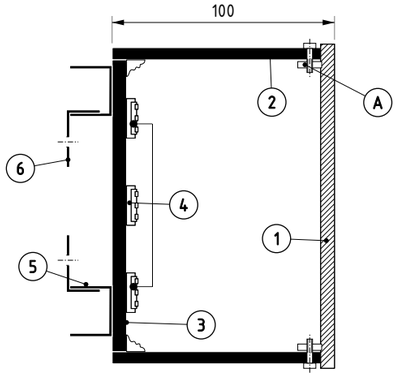

BILL OF MATERIALS (per 1 pcs.)

POS	PART	MATERIAL	FINISH	QTY (PERIMETER / AREA)
1	Letter face P6 (EXTRA, 7–23)	Plexi 3 mm white		24.79 m / 1.74 m²
1	Letter face P6+3 (X)	Plexi 3 mm white		6.37 m / 1.12 m²
	Front vinyl EXTRA + X	Vinyl foil, cast	3M 3630-33	1.41 + 1.12 m²
	Front vinyl 7–23	Vinyl foil, cast	3M 3630-125	0.33 m²
A	Fitting PVC edge	PVC 3 mm	–	31.16 m
B	Bolt, return to PVC edge		–	
2	Letter return EXTRA	Alu 1 mm	RAL 3020	17.56 m / 1.76 m²
2	Letter return 7–23	Alu 1 mm	RAL 1023	7.24 m / 0.72 m²
2	Letter return X	Alu 1 mm	RAL 3020	6.37 m / 0.64 m²
3	Letter back	Alu 1.5 mm	–	31.16 m / 2.87 m²
4	LED red / white 6500K		RED / 6500K	
5	Rail U 40x40x2 with ears (frame)	Aluminium	RAL 7035 matt	11.57 m
6	Mounting ear 40x40x2, ⌀8 hole	Aluminium	RAL 7035 matt	14 pcs. (0 extended)
7	Spacers 30 + 25 mm (X)		–	
8	Alu sheet ⌀1800 (X)	Alu 3 mm	RAL 1023	5.65 m / 2.53 m²
9	Trafo box, PWM + potentiometer			
10	Wall fixing		–	
11	Z strip 30x30x30x2 (on X sheet)	Alu	–	2 x 1080 = 2.16 m
12	Wallframe Z 30x30x30x2	Alu		2 x 1120 = 2.24 m
13	Wallframe tube 20x20x2	Alu		2 x 1008 = 2.02 m

MAIN DATA

Quantity	
Overall size	5603 x 1872
Profiles	P6 (EXTRA, 7–23) / P6+3 (X)
Letter depth	100
Face	White plexi + 3M translucent
Returns	RAL 3020 / RAL 1023 (7–23)
Alu sheet	3 mm, RAL 1023
X sheet mount	Z strips + welded wallframe 1160 x 1008
Rails	U 40x40x2 + ears, RAL 7035 matt
Illumination	LED red / white 6500K, dimmable
Environment	Exterior
Weight (calc.)	≈ 62 kg / pcs, excl. PSU

REVISIONS

REV	DESCRIPTION	DATE	BY
A	First issue	2026-10-07	

CLIENT

BrandFactory

TITLE

Illuminated letters P6 on rails + P6+3 on alu sheet, Z hang frame

ORDER NO.	FILE / DRAWING NO.			
	EXTRA FAS 1800U80 (7-23)			
SCALE (DIM. mm)	FORMAT	SHEET	REV.	PROJECTION
1:50 / 1:50	A3	1 / 1	A	
DRAWN	CHECKED	DATE		
		2026-10-07		