


FRONT VIEW


SCALE 1:10

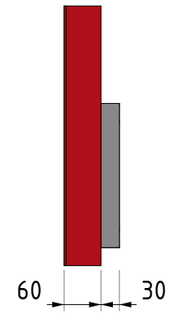

SIDE VIEW (RIGHT)

SCALE 1:10

P1 NON-LIT – no LED, plexi, cable or PSU

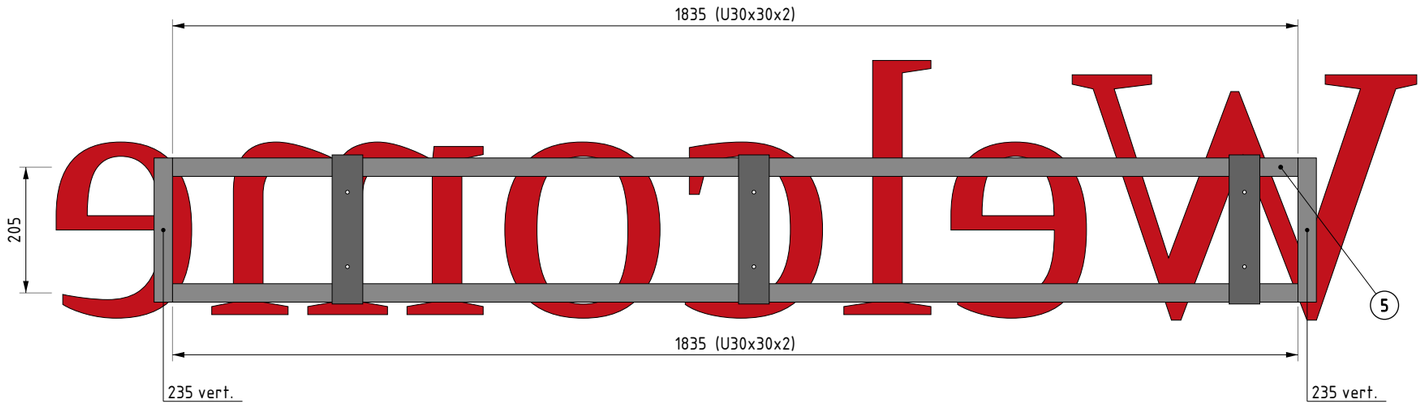

REAR VIEW (MIRRORED)


SCALE 1:10 | true view from the back



3D VIEW

ILLUSTRATIVE – NOT TO SCALE

PROFILE P1 ON RAILS – TYPICAL SECTION

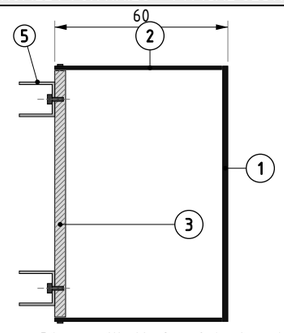

P1 – non-lit: Alu face 2 / return 1 / PVC back 10

BILL OF MATERIALS (per 1 pcs.)

POS	PART	MATERIAL	FINISH	QTY (PERIMETER / AREA)
1	Letter face P1	Alu 2 mm	RAL 3020	0.24 m²
2	Letter return	Alu 1 mm	RAL 3020	12.85 m / 0.77 m²
3	Letter back	PVC 10 mm	RAL 3020	12.85 m / 0.24 m²
4	Wallframe U 30x30x2	Aluminium		4.14 m
5	Wall fixing		-	
6	Hanger U 243x50, fl. 33	Alu 3 mm		3 pcs.

MAIN DATA

Quantity	
Overall size	2218 x 423
Profile	P1 on wallframe
Letter depth	60
Face	Alu 2 mm, RAL 3020
Returns	RAL 3020
Font	Times New Roman
Rails	U 30x30x2 + hangers, RAL ____
Illumination	NONE – P1, no LED / plexi
Environment	Exterior
Weight (calc.)	≈ 9.1 kg / pcs, excl. PSU

REVISIONS

REV	DESCRIPTION	DATE	BY
A	First issue	2026-10-13	

CLIENT

TEST


TITLE

Welcome – P1 non-lit letters on wallframe

ORDER NO.	FILE / DRAWING NO.
ALT0000_00.00_RS	TEST Welcome P1


SCALE (DIM. mm)	FORMAT	SHEET	REV.	PROJECTION
1:10 / 1:10	A3	1 / 2	A	

DRAWN	CHECKED	DATE
		2026-10-13

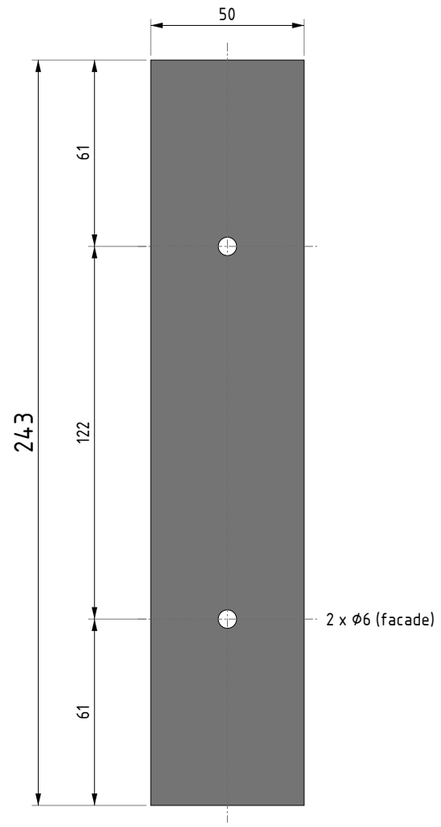


VIEW FROM FACADE

SCALE 1:2

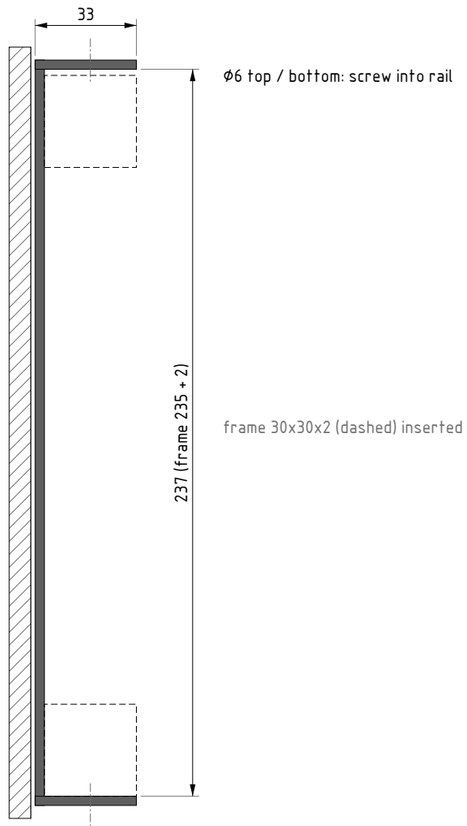

SIDE VIEW

SCALE 1:2

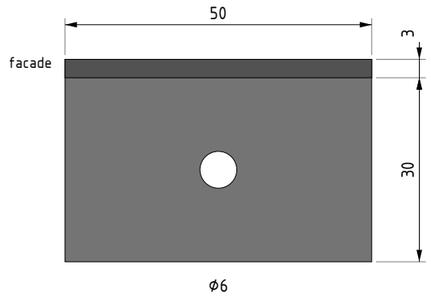

TOP VIEW

SCALE 1:1

NOTES

1. Hangers fixed to facade first (facade = concrete unless specified), frame inserted, screwed to each hanger at top and bottom (Ø6).
2. Material Alu 3 mm (steel for heavy signs).
3. Inside = frame 235 + 2; frame rests on bottom flange.
4. Final screw positions – by production.
5. Positions: see rear view, sheet 1.

BILL OF MATERIALS – HANGERS (per 1 sign)

POS	PART	MATERIAL	FINISH	QTY (PERIMETER / AREA)
1	Hanger U 243 x 50, flanges 33	Alu 3 mm		3 pcs.
2	Facade anchor for Ø6 hole	-	-	6 pcs.
3	Screw flange -> rail (Ø6)	-	-	6 pcs.

MAIN DATA

Height	243 (inside frame 235 + 2)
Width	50
Flanges	33 (rail 30 + 3)
Material	Alu 3 mm
Facade holes	2 x Ø6
Flange holes	1 x Ø6 top, 1 x Ø6 bottom
Quantity	3 pcs.
Weight (calc.)	≈ 0.13 kg / pcs

REVISIONS

REV	DESCRIPTION	DATE	BY
A	First issue	2026-10-13	

CLIENT: **TEST**

TITLE: Hangers (U) – Welcome – P1 non-lit letters on wallframe

ORDER NO.: **ALT0000_00.00_RS**

FILE / DRAWING NO.: TEST Welcome P1

SCALE (DIM. mm)	FORMAT	SHEET	REV.	PROJECTION
1:2 / 1:1	A3	2 / 2	A	

DRAWN	CHECKED	DATE
		2026-10-13